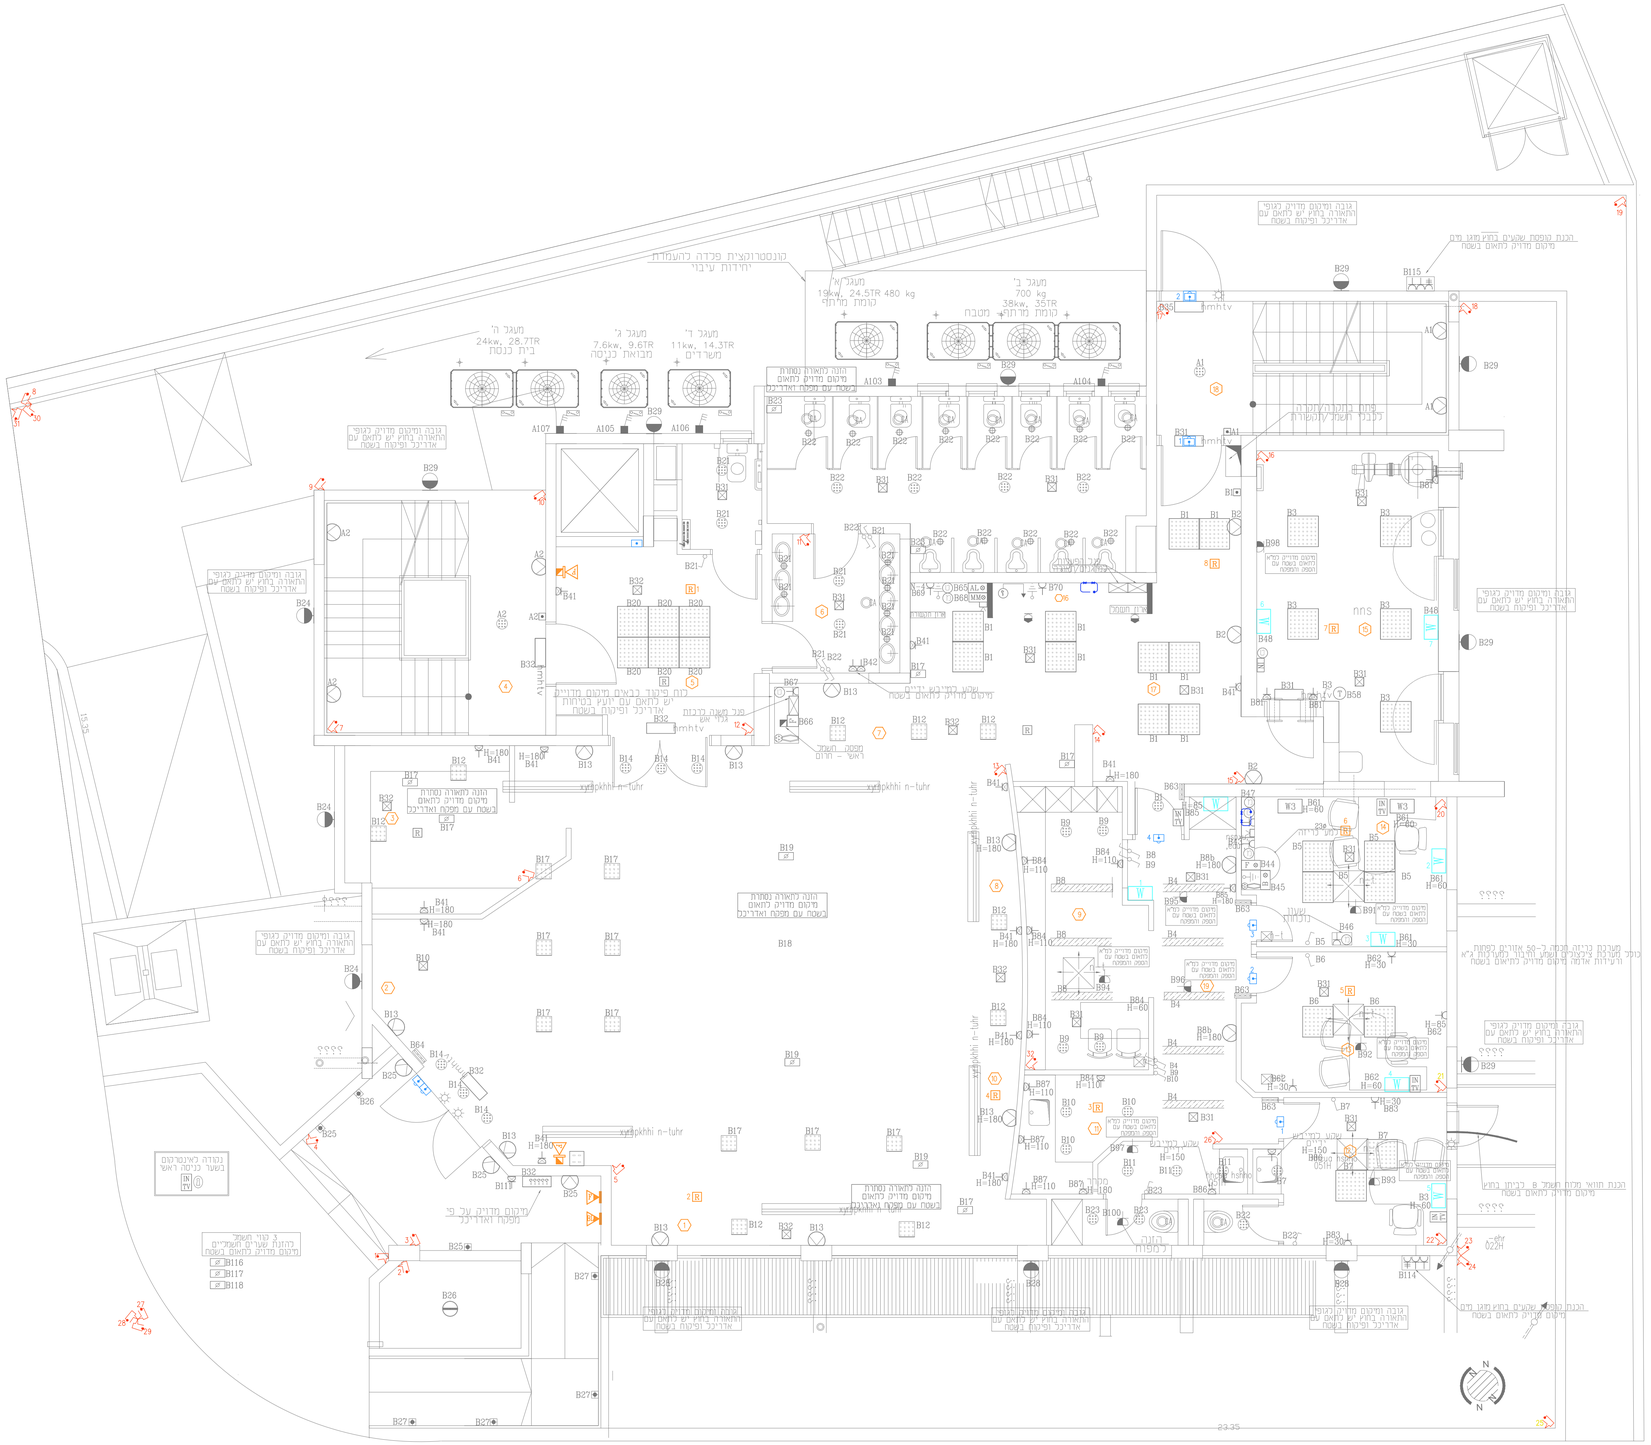
מעגל א'
19kw, 24.5TR 480 kg
קומת מרתף
מעגל ב'
700 kg
38kw, 35TR
קומת מרתף
מטבח
מעגל ה'
24kw, 28.7TR
בית כנסת
מעגל ג'
7.6kw, 9.6TR
מבואות כניסה
מעגל ד'
11kw, 14.3TR
משרדים
קונסטרוקציית פלדה כהעמדת יחידות עיבוי
מקום בתקרה עליה לגבבי תשמל/תקשורת
מקום מדיה לאולם בשמה
מקום מדיה לאולם בשמה עם מפסק ואדריכל
מקום מדיה לאולם בשמה עם מפסק ואדריכל
מקום מדיה לאולם בשמה עם מפסק ואדריכל